
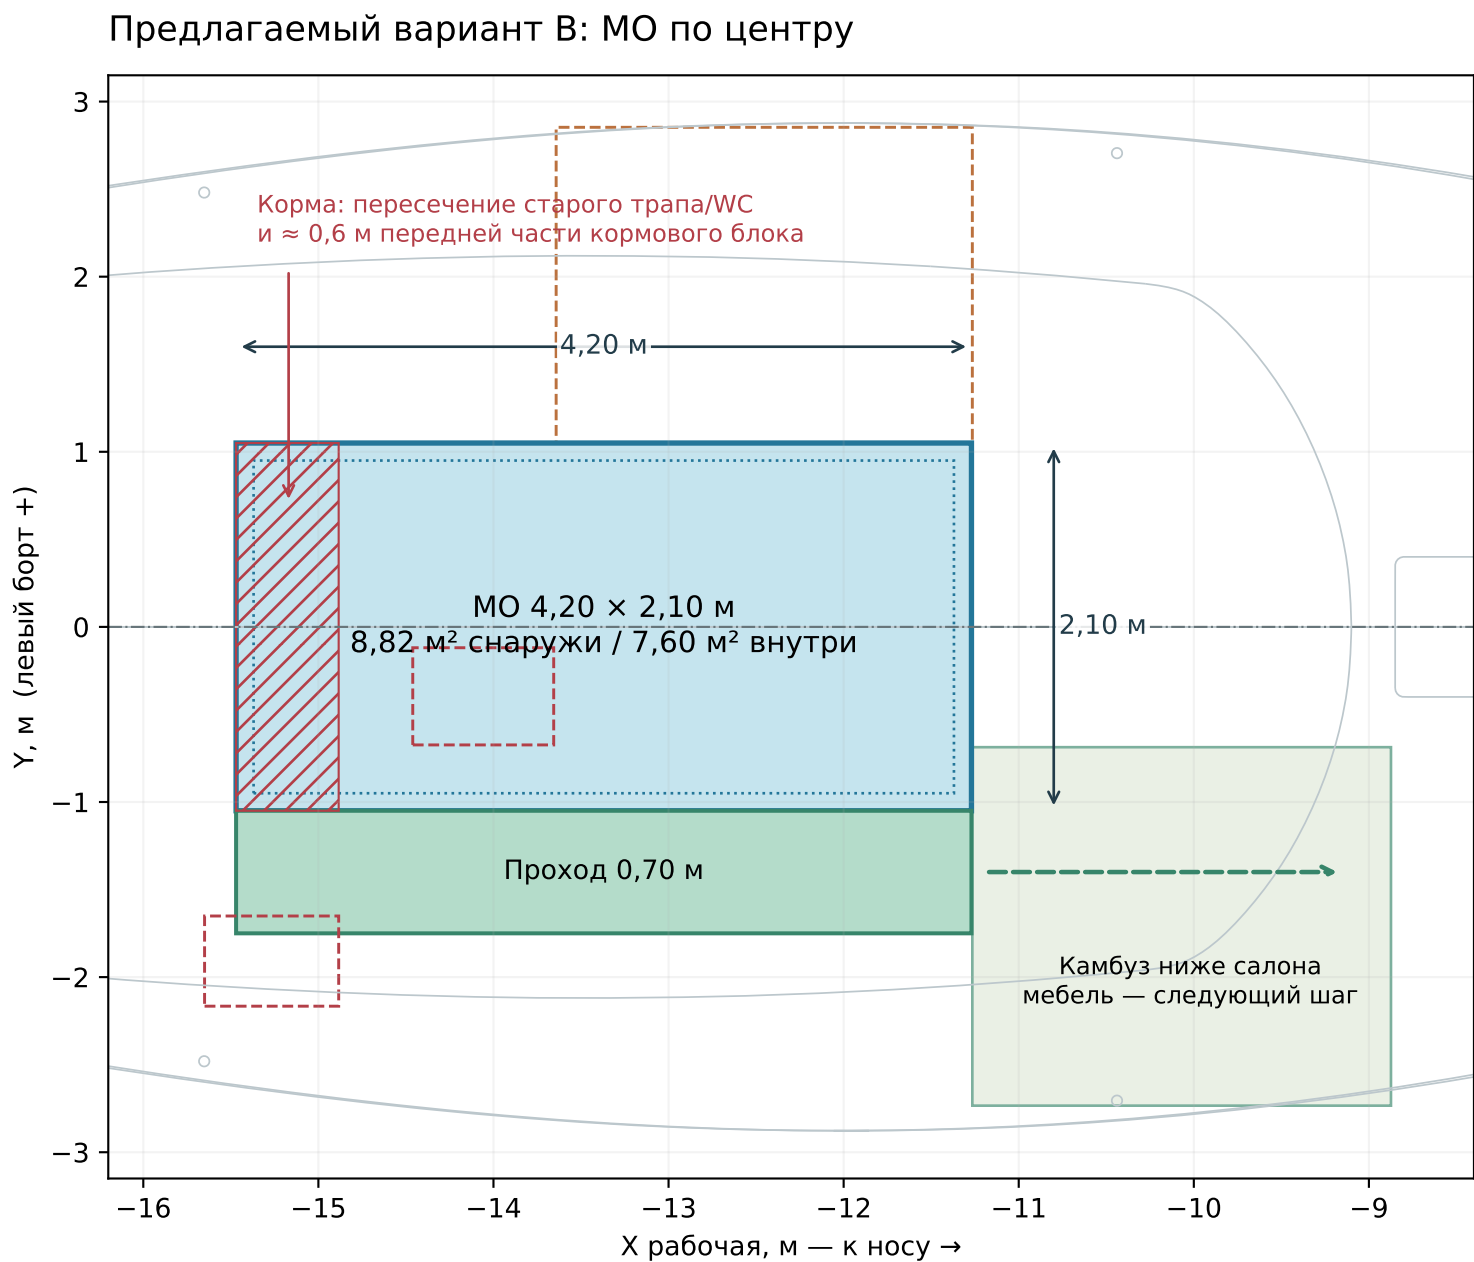


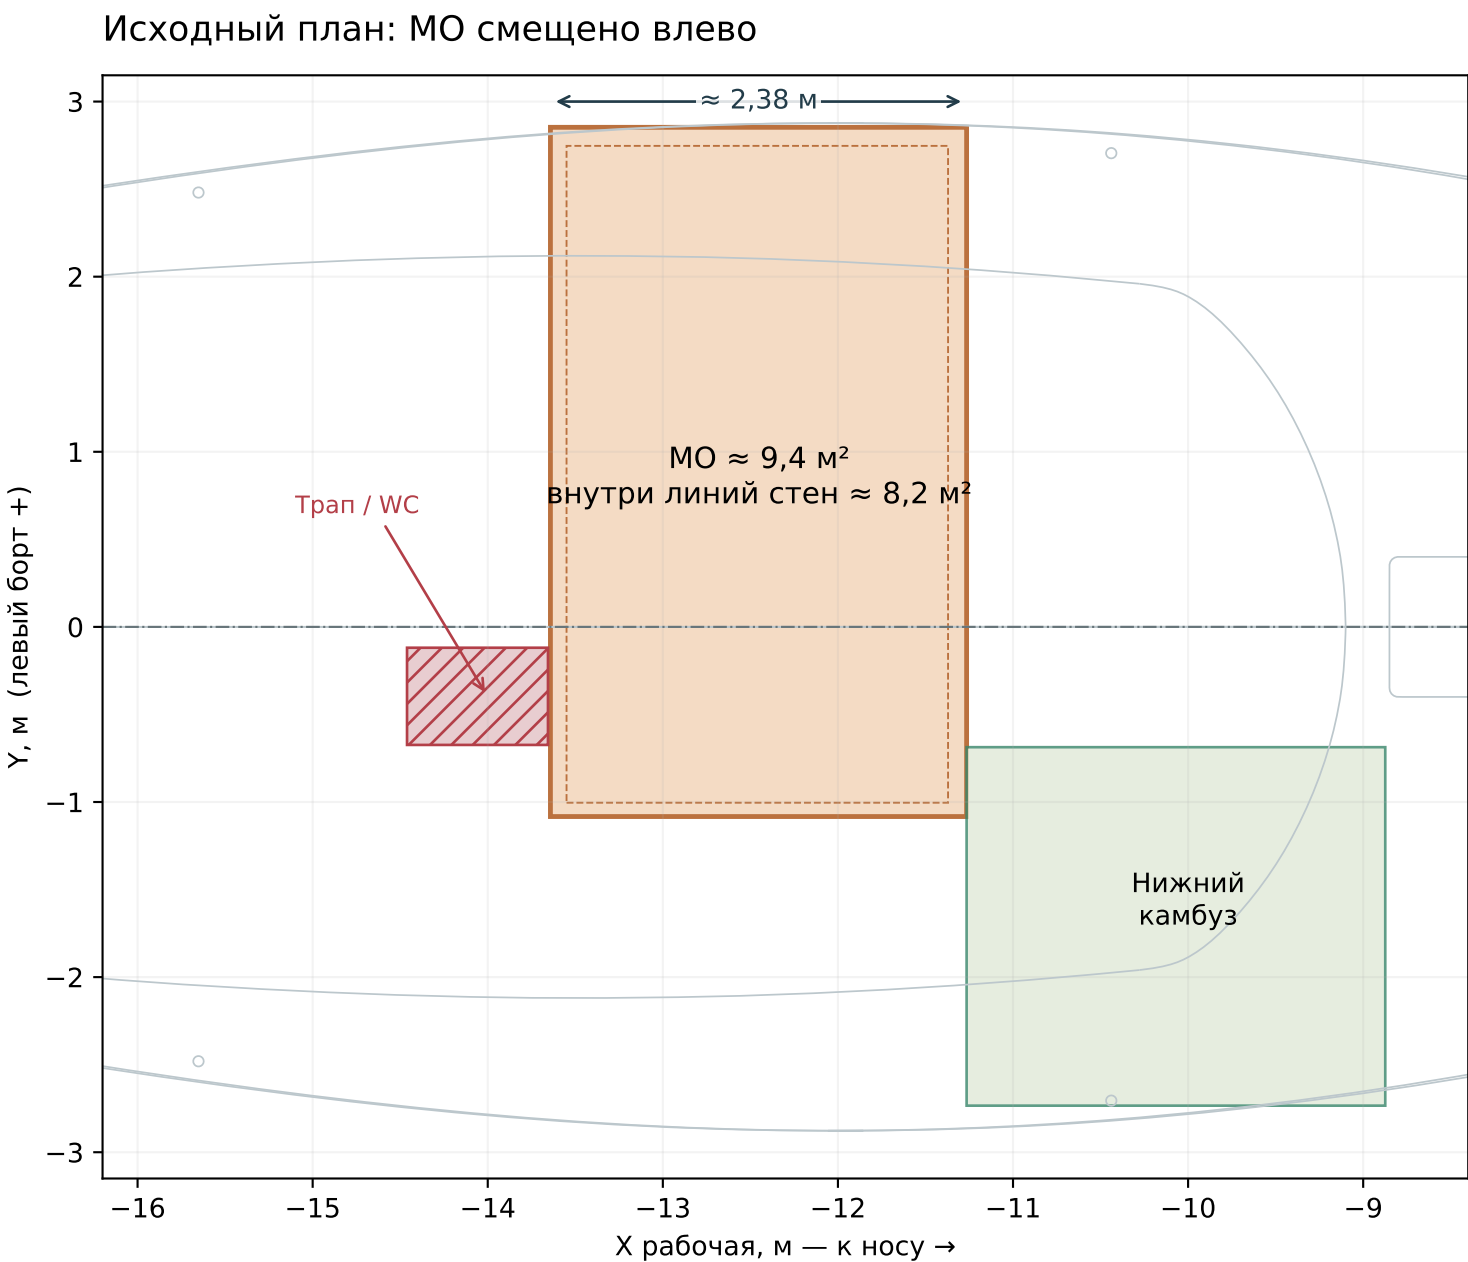


Вариант	Наружный габарит, м	Пятно, м^2	Внутри стен, м^2	Главное условие
Исходный GA	$\approx 2,38 \times 3,94$	$\approx 9,36$	$\approx 8,18$	Пайол и чистая высота не установлены
А, проверен	$3,60 \times 2,60$	9,36	8,16	Проход $0,75 \text{ м}$: местами лишь $\approx 1,69 \text{ м}$ высоты
В, для дальнейшей проработки	$4,20 \times 2,10$	8,82	7,60	МО $\approx 1,47 \text{ м}$; проход $0,70 \text{ м}$ требует проёма сверху

Серый — проекция исходных кромок, не чистая внутренняя граница. Оранжевый пунктир — исходное МО. Красный — коллизии.

GA привязан по носу приблизительно (положение $\pm 0,2 \text{ м}$). Вариант В не подтверждает размещение агрегатов, проход через двери или прочность.

Высота: два уровня и открытый боковой проход

Контур сечения G02: X ≈ −12,25 м • уровни пола/перекрытия предложены, не взяты из исполнительного чертежа

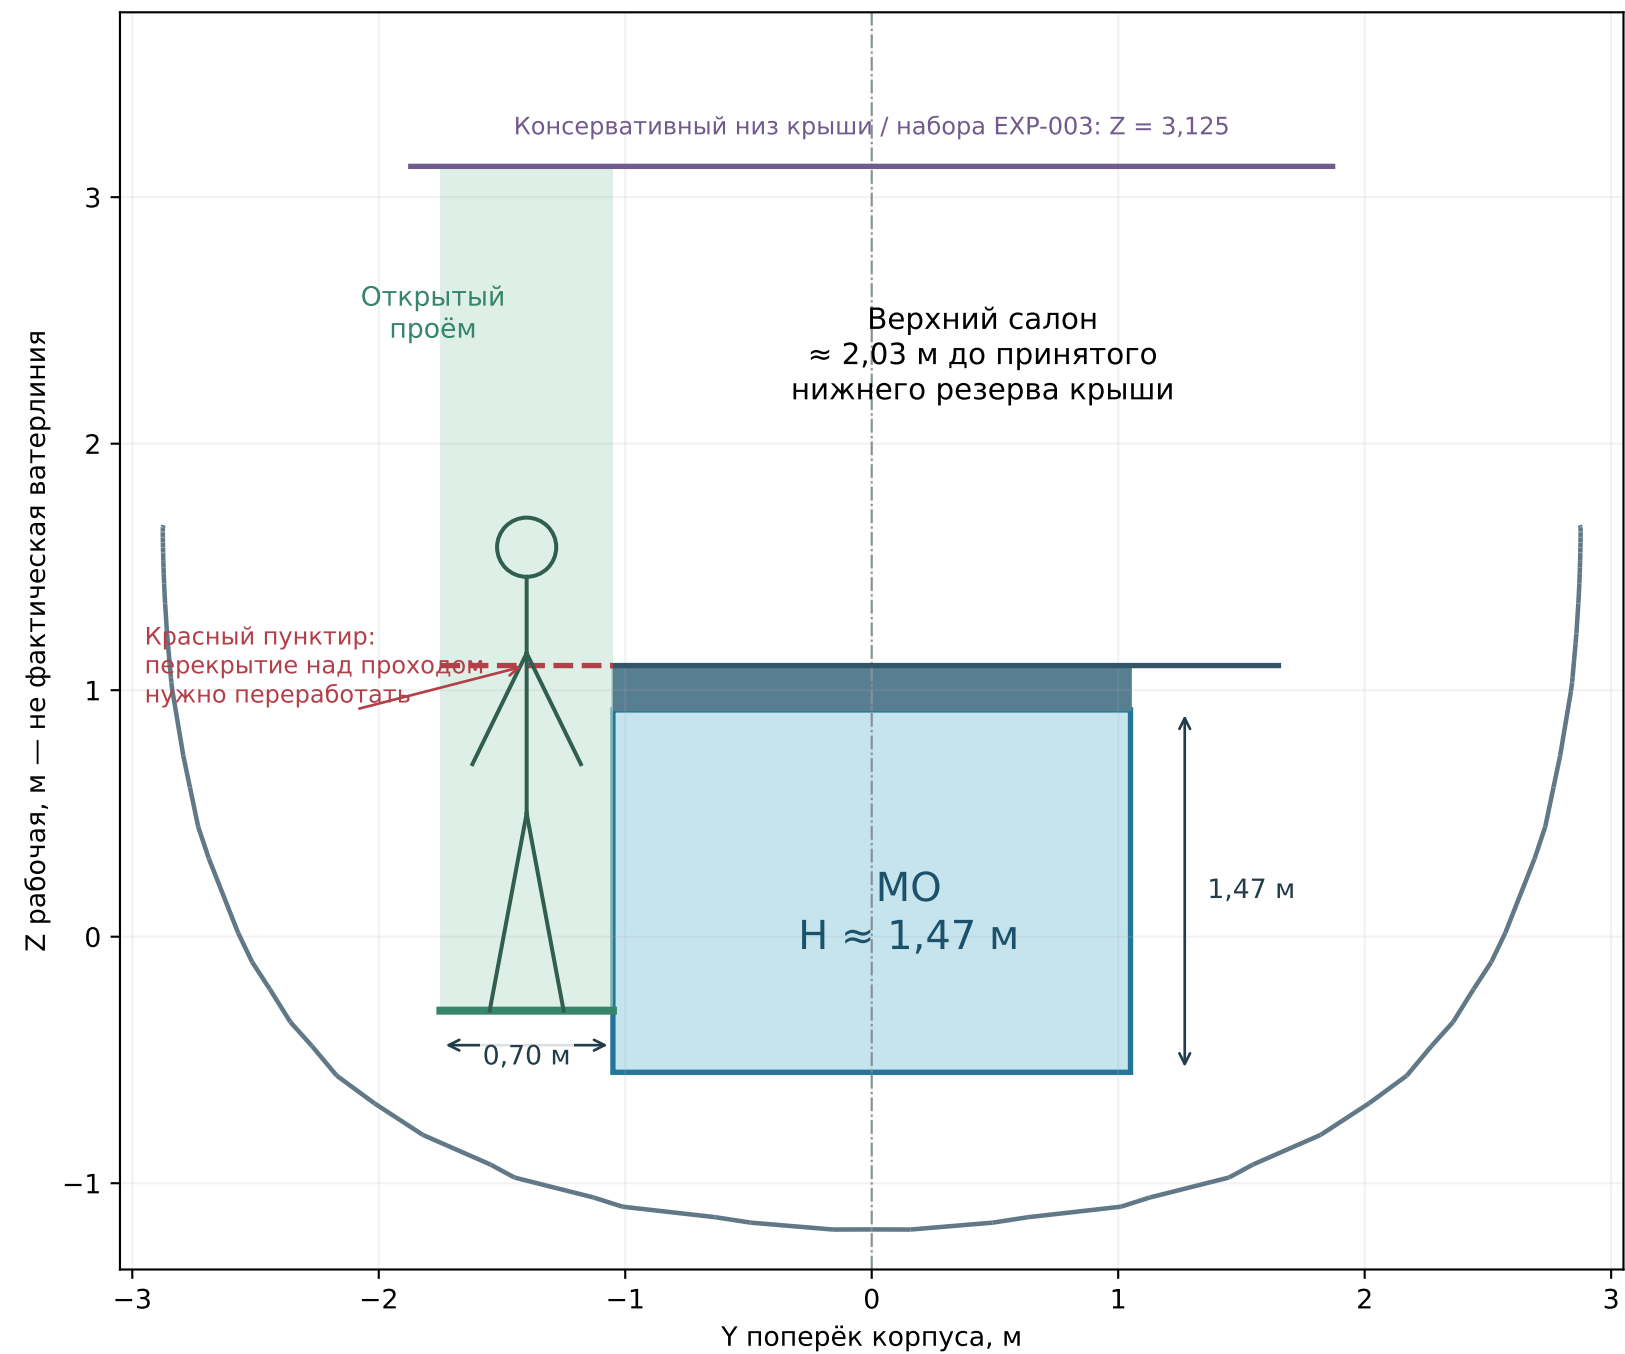

РАСЧЁТНЫЕ УРОВНИ

Пайол МО: -0.55 м
Низ перекрытия: 0.92 м
Пол салона: 1.10 м
Перекрытие: 0.18 м
Пайол прохода: -0.30 м

ПЛОЩАДЬ И ВЫСОТА

$4,00 \times 1,90 = 7,60 \text{ м}^2$ внутри стен
 $0,92 - (-0,55) = 1,47 \text{ м}$
Геометрический объём $\approx 11,2 \text{ м}^3$

Это объём до размещения агрегатов, фундаментов, труб и сервисных зон.

У прохода запас до условного внутреннего края крыши — лишь 0,02 м. Стойки, ограждение и зазоры ещё не спроектированы.

Почему не 2 м в МО: над ним сохранён верхний салон. Для 2 м при том же пайоле его пол нужно поднять на 0,53 м; тогда сверху останется около 1,50 м. Два полноценных уровня по 2 м потребуют отдельного изменения надстройки.

Проверка днища выполнена по сетке исторической оболочки. Резерв под пайолом 0,15 м, стен 0,10 м и перекрытия 0,18 м — допущения.

Разрез показывает предложенное открытие объёма над проходом; существующее перекрытие не объявлено уже вырезанным.

Внешняя крыша EXP-003 сохранена. Продольная схема, новый трап, WC, границы кормовой каюты, вал и силовые связи требуют следующей итерации.