


LENGTH O.A.	20.50 m
LENGTH W.L.	17.50 m
BEAM	5.75 m
DRAFT	— m

DISPLACEMENT	— ton
BALLAST	— ton

MAINSAIL	131.0 m2
JIB	110.0 m2
TOTAL	241.0 m2

STORMJIB	50.0 m2
TRYSAIL	39.0 m2
REACHER	185.0 m2

I	29.00 m
J	8.00 m
P	26.00 m
E	9.10 m

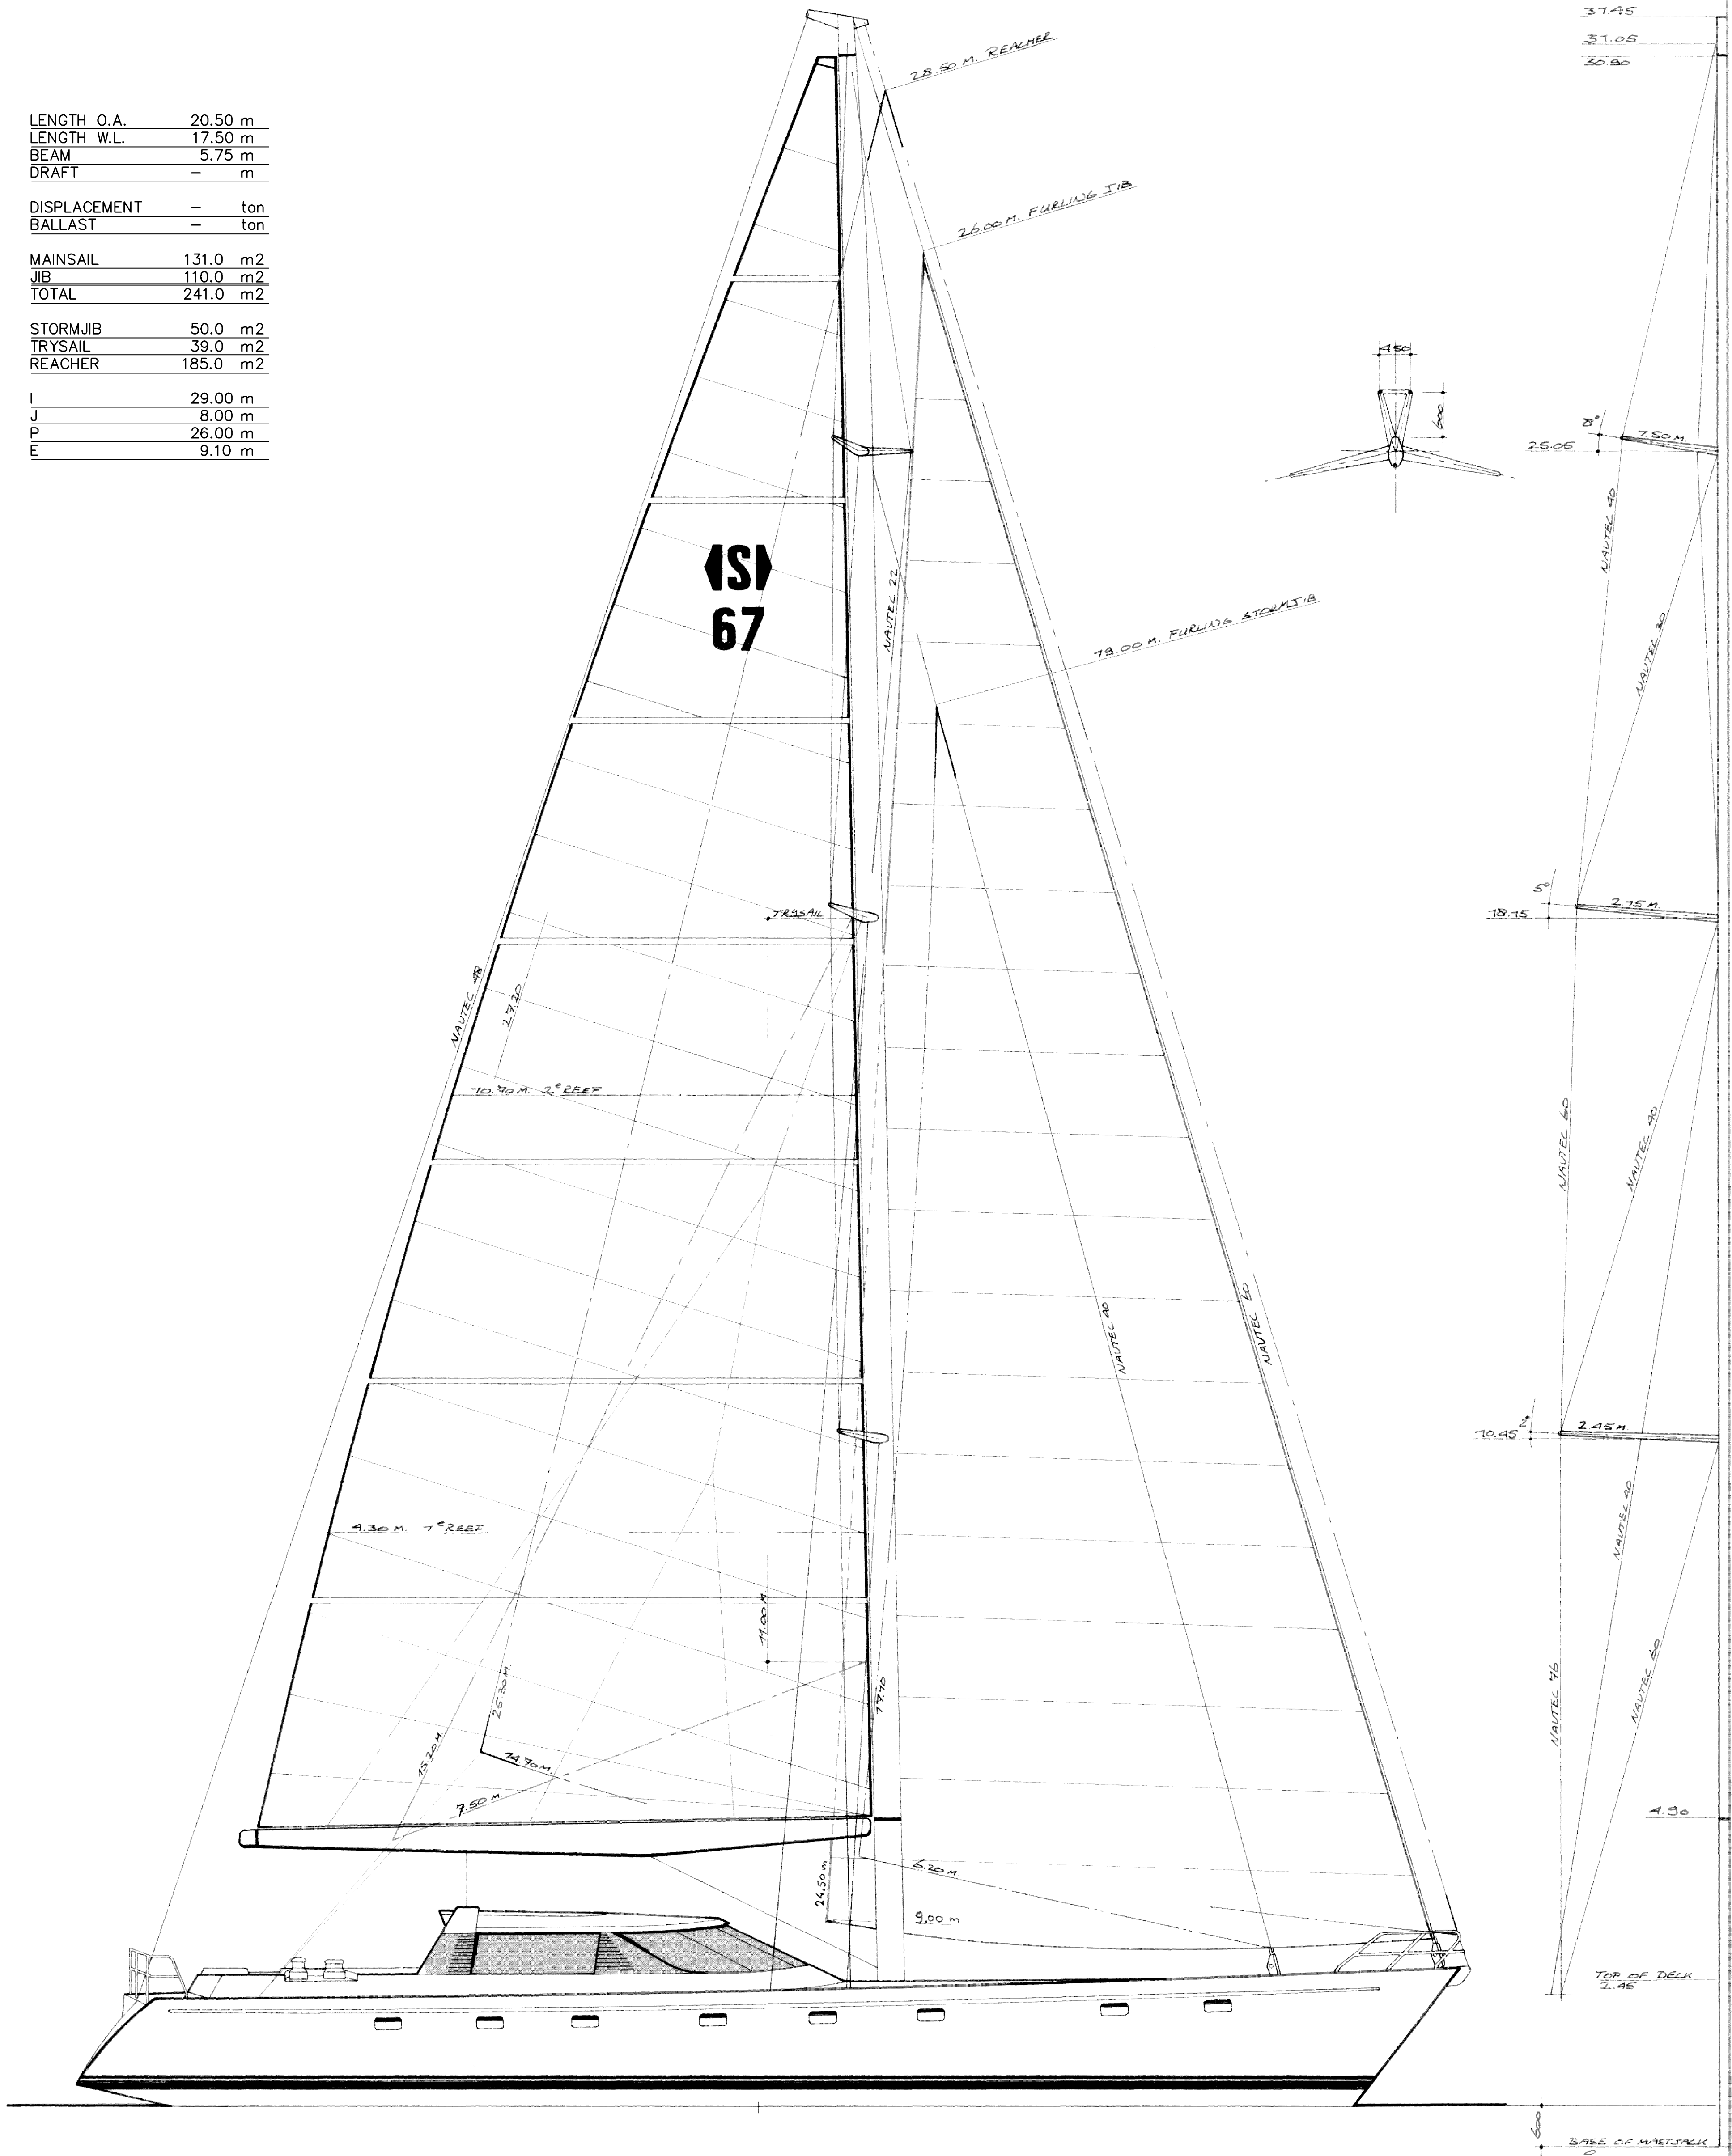

ALL RIGHTS OF THIS DESIGN
AND DETAILS ARE RESERVED

It is sent to you for personal
use authorized in writing by our
firm. Copy or inspection by a third
party or any work other than
authorized is forbidden and will be
considered an infringement of
these rights.

DATE:	ALTERATION:	
VAN DE STADT DESIGN E.G. VAN DE STADT & PARTNERS BV POSTBUS 193 1520 AD WORMERVEER HOLLAND		
SAILPLAN		SCALE: 1:50
VAN DE STADT 67		HK
For: RT-Yachtbau Mr. M. Possekel		DATE: 21/05/2001
		NO.: 430A-8-1